



Republika e Kosovës
Republika Kosova-Republic of Kosova
Qeveria -Vlada-Government

Ministria e Mjedisit dhe Planifikimit Hapësinor /Ministarstvo Sredine i Prostornog Planiranja/Ministry of Environment and Spatial Planning
AGJENCIA KADASTRALE E KOSOVËS/ KATASTARSKA AGENCIJA KOSOVA/ KOSOVA CADASTRAL AGENCY

Zyra kadastrale komunale / Opštinska katastarska kancelarija: Ferizaj


Nr. i njësisë kadastrale / Br. katastarske jedinice : 01231-0
242/2026

Zona kadastrale / Katastarska zona: Zaskok

Numri i lëndës / Broj predmeta: 279/1172-140/26

Lloji i njësisë kadastrale / Vrsta katastarske jedinice : Parcel

Shkalla e zvoglimit / Razmera plana : 1:750

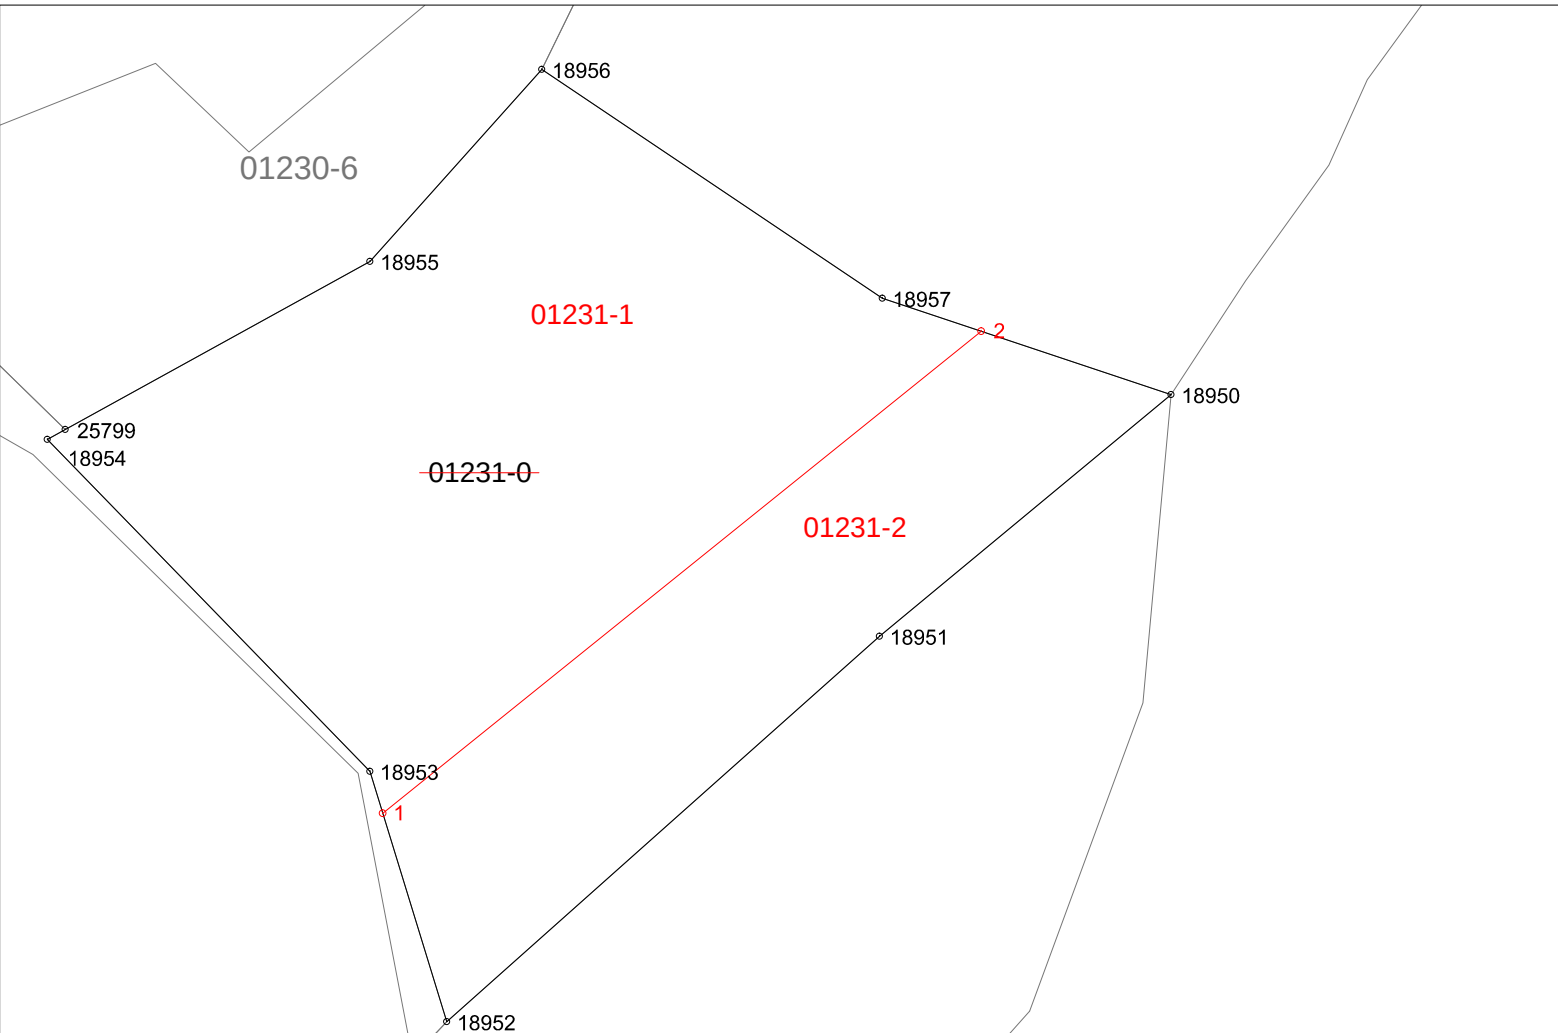

Nr	Y	X	H	Kodi	Përshkrimi	Burimi
FE01-PM	7510693.828	4691608.088	659.610	11	Monoment	PM
1	7511242.639	4687965.268	757.802	2	Kunjë - shtyllë metalik	PM
2	7511302.001	4688013.076	738.920	2	Kunjë - shtyllë metalik	PM
18950	7511320.843	4688006.803	739.546	2	Kunjë - shtyllë metalik	PM
18951	7511291.923	4687982.845	751.788	2	Kunjë - shtyllë metalik	PM
18952	7511248.993	4687944.607	764.344	2	Kunjë - shtyllë metalik	PM
18953	7511241.354	4687969.446	755.520	2	Kunjë - shtyllë metalik	PM
18954	7511209.385	4688002.356	737.170	2	Kunjë - shtyllë metalik	PM
18955	7511241.374	4688020.015	732.441	2	Kunjë - shtyllë metalik	PM
18956	7511258.414	4688039.044	722.600	2	Kunjë - shtyllë metalik	PM
18957	7511292.184	4688016.344	737.318	2	Kunjë - shtyllë metalik	PM
25799	7511211.142	4688003.326	736.803	2	Kunjë - shtyllë metalik	PM

Rilevoi / Snimio: LIRIDON SEJDIU
(emri dhe mbiemri i gjeodetit/kompanisë/ ime i prezime geodeta/ kompanije)

Aprovoi / Usvojio: _____
(emri dhe mbiemri i përsorit zyrtar/ ime i prezime sluzbenog lica)

Nr. i licencës / Br. licence: 140

V.V.

Nënshkrimi / Potpis: _____

Nënshkrimi / Potpis: _____

Data e rilevimit / Datum snimanja: 18.09.2026

Data e aprovimit / Datum usvajanja: _____