



Republika e Kosovës
Republika Kosova-Republic of Kosova
Qeveria -Vlada-Government

Ministria e Mjedisit dhe Planifikimit Hapësinor /Ministarstvo Sredine i Prostornog Planiranja/Ministry of Environment and Spatial Planning
AGJENCIA KADASTRALE E KOSOVËS/ KATASTARSKA AGENCIJA KOSOVA/ KOSOVA CADASTRAL AGENCY

Zyra kadastrale komunale / Opštinska katastarska kancelarija: Ferizaj


Nr. i njësisë kadastrale / Br. katastarske jedinice : 01123-0
240/2026

Zona kadastrale / Katastarska zona: Zaskok

Numri i lëndës / Broj predmeta: 277/1172-140/26

Lloji i njësisë kadastrale / Vrsta katastarske jedinice : Parcel

Shkalla e zvoglimit / Razmera plana : 1:750

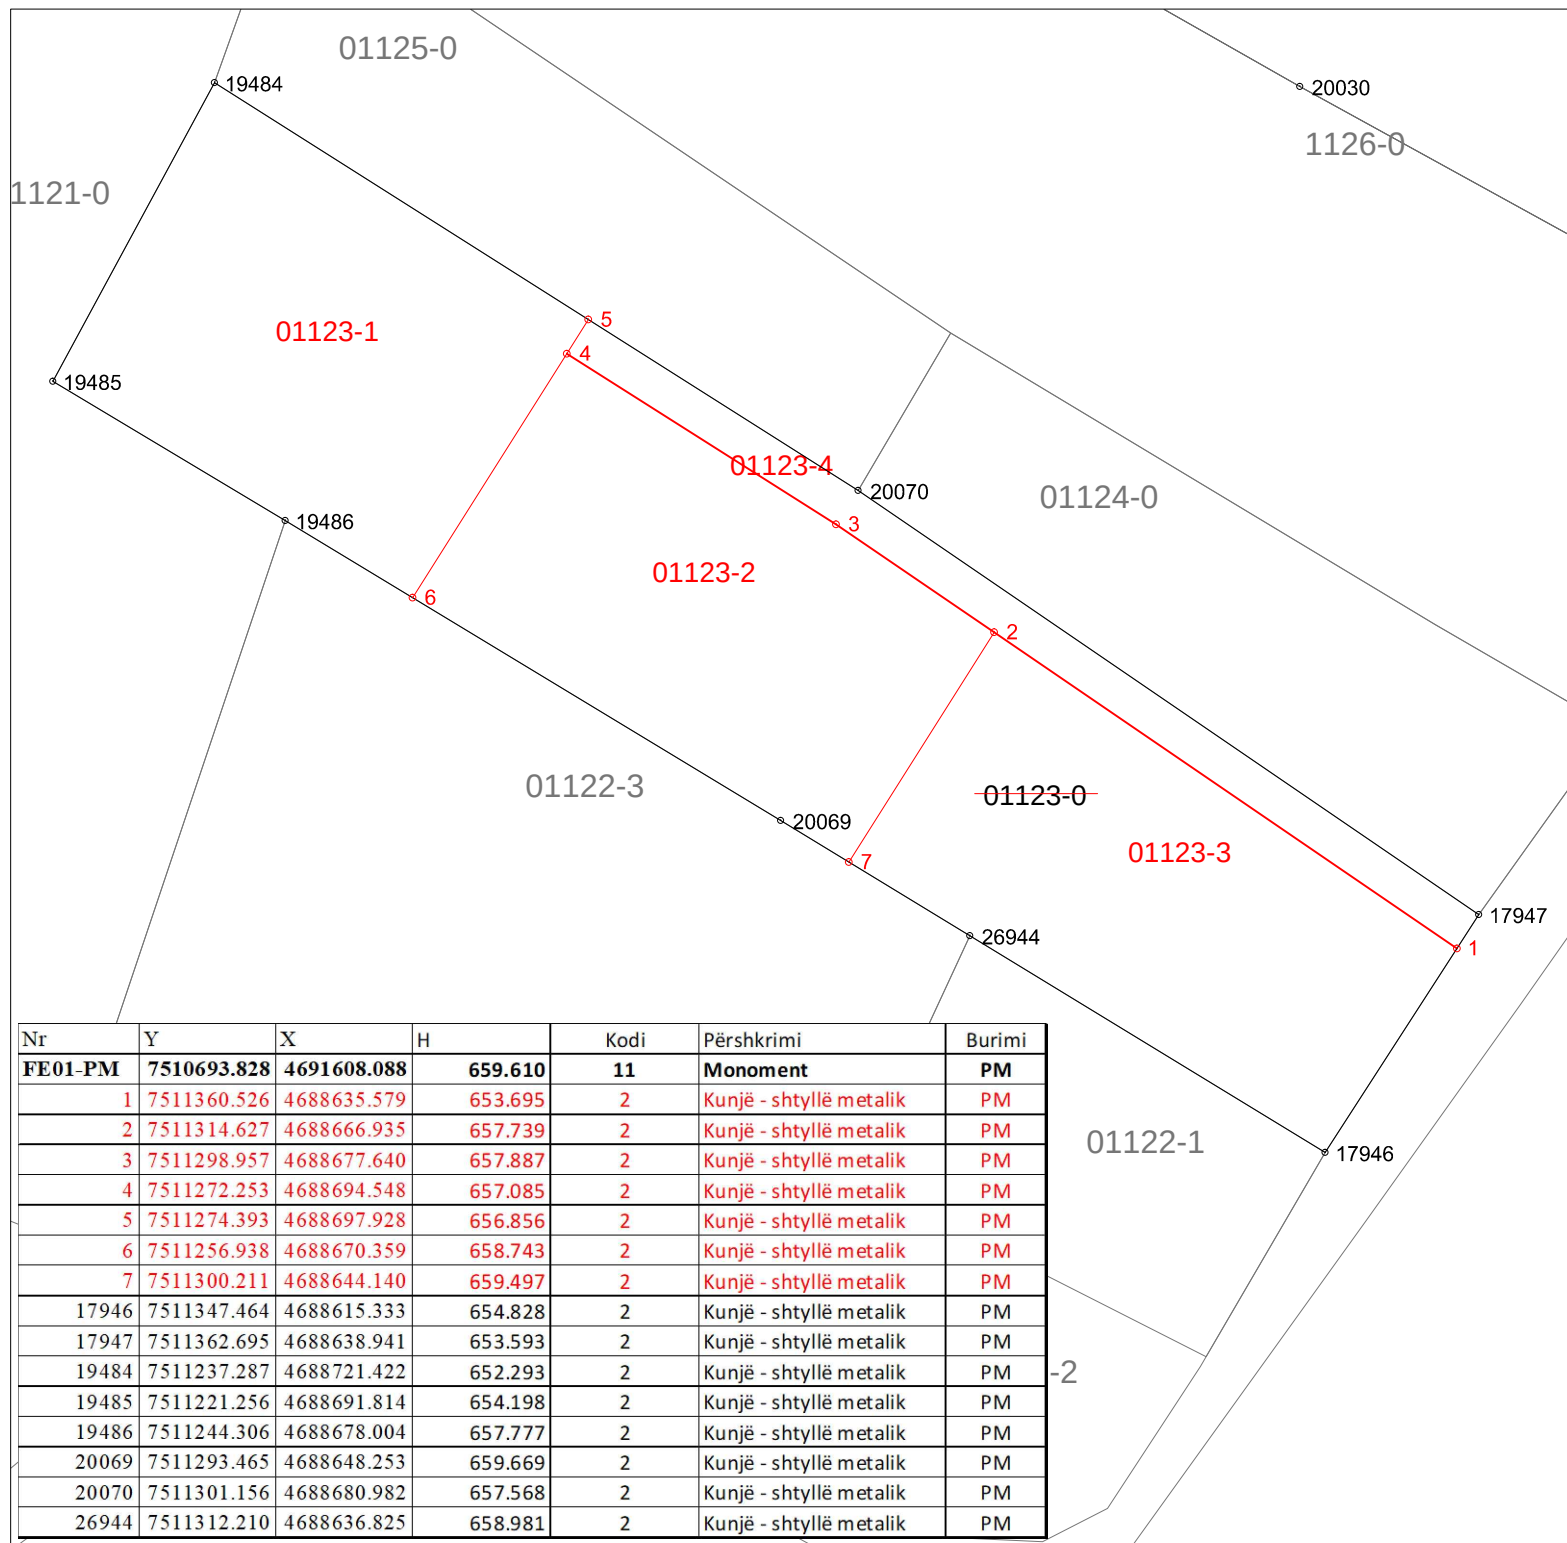

Nr	Y	X	H	Kodi	Përshkrimi	Burimi
FE01-PM	7510693.828	4691608.088	659.610	11	Monoment	PM
1	7511360.526	4688635.579	653.695	2	Kunjë - shtyllë metalik	PM
2	7511314.627	4688666.935	657.739	2	Kunjë - shtyllë metalik	PM
3	7511298.957	4688677.640	657.887	2	Kunjë - shtyllë metalik	PM
4	7511272.253	4688694.548	657.085	2	Kunjë - shtyllë metalik	PM
5	7511274.393	4688697.928	656.856	2	Kunjë - shtyllë metalik	PM
6	7511256.938	4688670.359	658.743	2	Kunjë - shtyllë metalik	PM
7	7511300.211	4688644.140	659.497	2	Kunjë - shtyllë metalik	PM
17946	7511347.464	4688615.333	654.828	2	Kunjë - shtyllë metalik	PM
17947	7511362.695	4688638.941	653.593	2	Kunjë - shtyllë metalik	PM
19484	7511237.287	4688721.422	652.293	2	Kunjë - shtyllë metalik	PM
19485	7511221.256	4688691.814	654.198	2	Kunjë - shtyllë metalik	PM
19486	7511244.306	4688678.004	657.777	2	Kunjë - shtyllë metalik	PM
20069	7511293.465	4688648.253	659.669	2	Kunjë - shtyllë metalik	PM
20070	7511301.156	4688680.982	657.568	2	Kunjë - shtyllë metalik	PM
26944	7511312.210	4688636.825	658.981	2	Kunjë - shtyllë metalik	PM

Rilevoi / Snimio: LIRIDON SEJDIU
(emri dhe mbiemri i gjeodetit/kompanisë/ ime i prezime geodeta/ kompanije)

Aprovoi / Usvojio: _____
(emri dhe mbiemri i përsosur zyrtar/ ime i prezime shërbëtor ligj)

Nr. i licencës / Br. licence: 140

V.V.

Nënshkrimi / Potpis: _____

Nënshkrimi / Potpis: _____

Data e rievimit / Datum snimanja: 18.09.2026

Data e aprovimit / Datum usvajanja: _____