Republika e Kosovës
Republika Kosova-Republic of Kosova
Qeveria -Vlada-Government
Ministria e Mjedisit dhe Planifikimit Hapësinor /Ministarstvo Sredine i Prostornog Planiranja/Ministry of Environment and Spatial Planning
AGJENCIA KADASTRALE E KOSOVËS/ KATASTARSKA AGECIJA KOSOVA/ KOSOVA CADASTRAL AGENCY

Zyra kadastrale komunale / Opštinska katastarska kancelarija: Ferizaj


Zona kadastrale / Katastarska zona: Zaskok

Lloji i njësisë kadastrale / Vrsta katastarske jedinice : Parcel

Nr. i njësisë kadastrale / Br. katastarske jedinice : 01209-0,01210-0, 01211-0

Numri i lëndës / Broj predmeta: 241/2026 278/1172-140/26_1

Shkalla e zvoglimit / Razmera plana : 1:1000

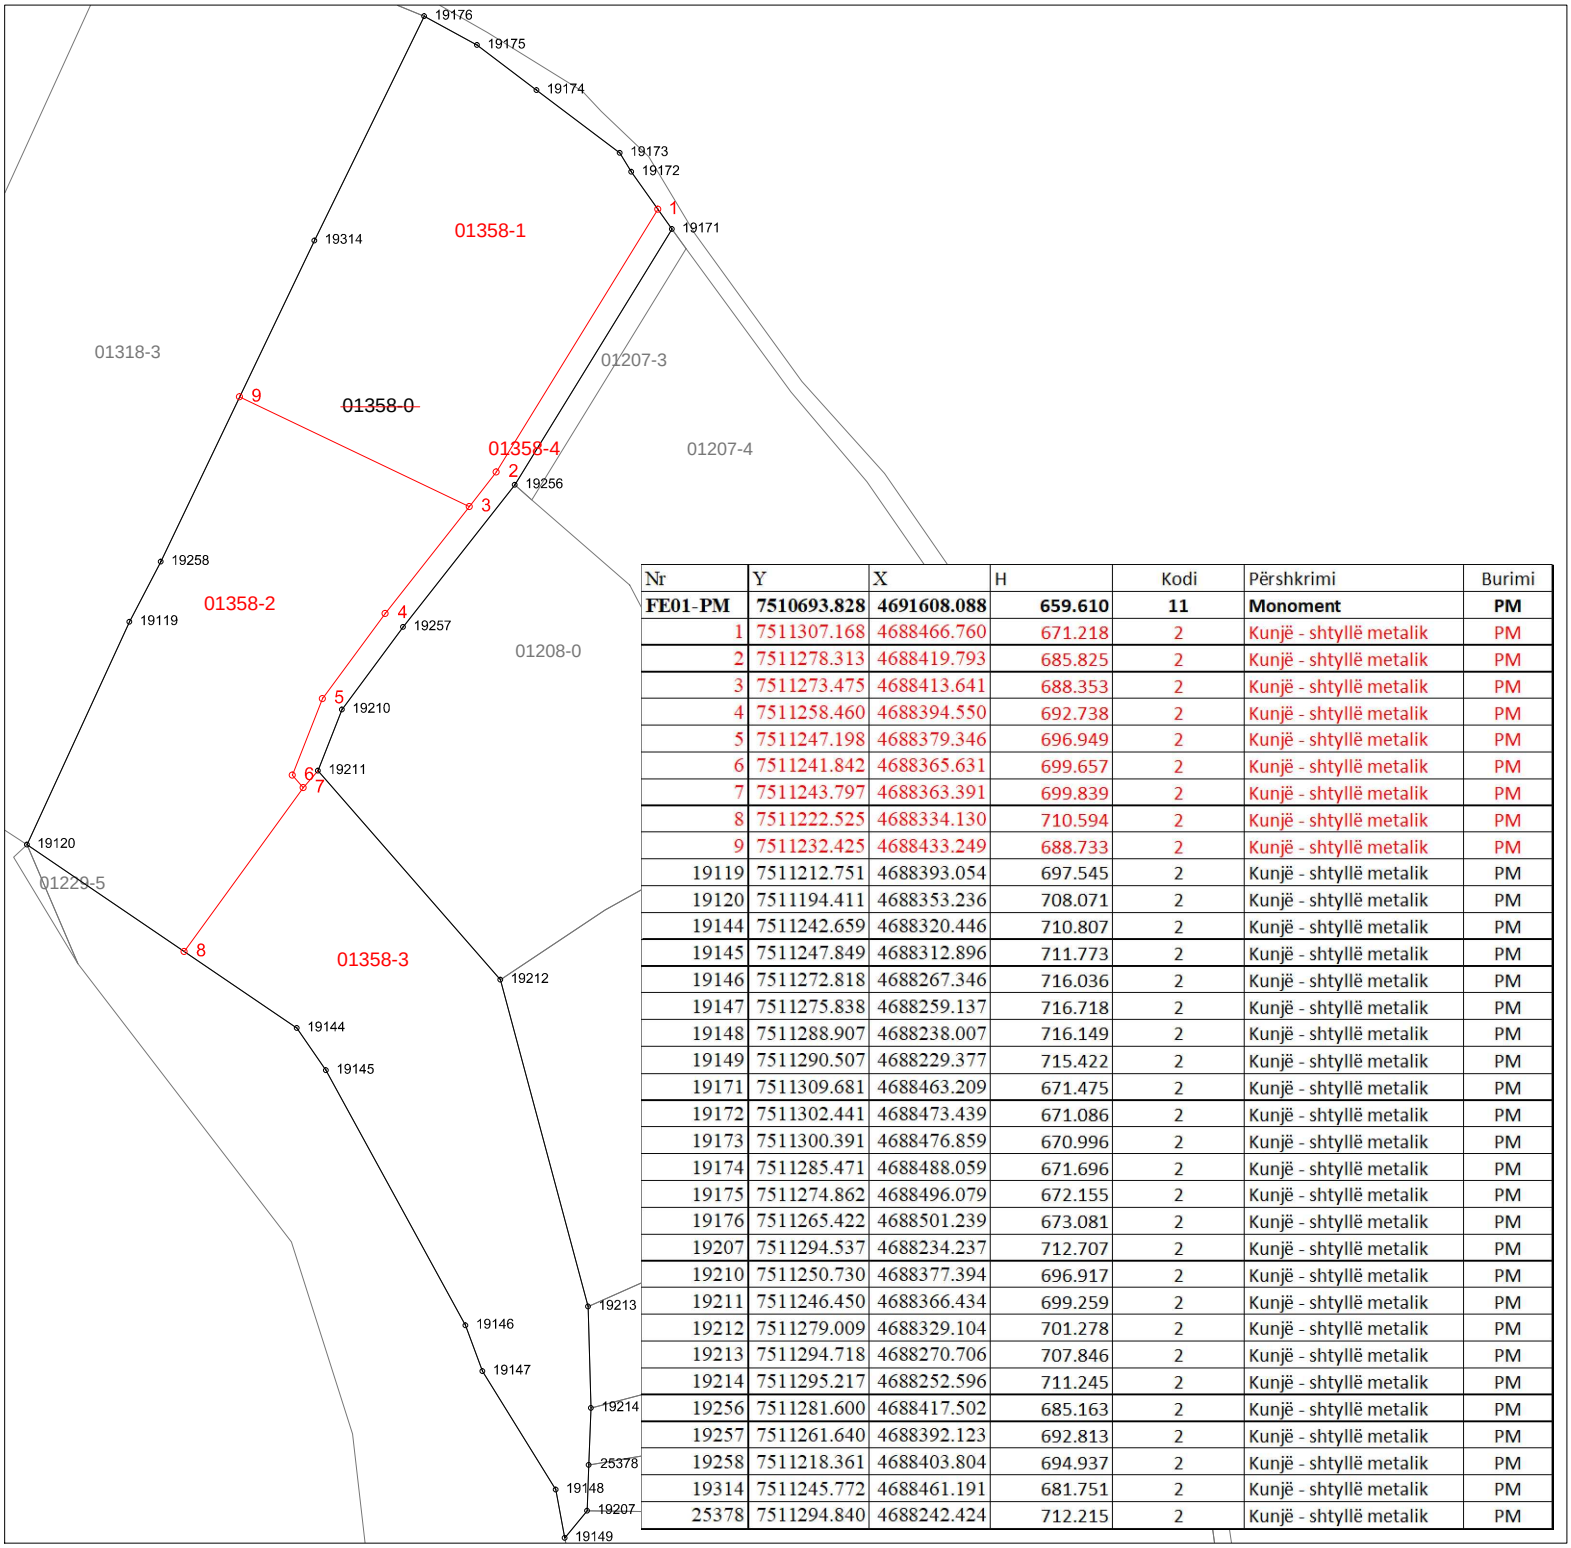

Nr	Y	X	H	Kodi	Përshkrimi	Burimi
FE01-PM	**7510693.828**	**4691608.088**	**659.610**	**11**	**Monoment**	**PM**
1	7511307.168	4688466.760	671.218	2	Kunjë - shtyllë metalik	PM
2	7511278.313	4688419.793	685.825	2	Kunjë - shtyllë metalik	PM
3	7511273.475	4688413.641	688.353	2	Kunjë - shtyllë metalik	PM
4	7511258.460	4688394.550	692.738	2	Kunjë - shtyllë metalik	PM
5	7511247.198	4688379.346	696.949	2	Kunjë - shtyllë metalik	PM
6	7511241.842	4688365.631	699.657	2	Kunjë - shtyllë metalik	PM
7	7511243.797	4688363.391	699.839	2	Kunjë - shtyllë metalik	PM
8	7511222.525	4688334.130	710.594	2	Kunjë - shtyllë metalik	PM
9	7511232.425	4688433.249	688.733	2	Kunjë - shtyllë metalik	PM
19119	7511212.751	4688393.054	697.545	2	Kunjë - shtyllë metalik	PM
19120	7511194.411	4688353.236	708.071	2	Kunjë - shtyllë metalik	PM
19144	7511242.659	4688320.446	710.807	2	Kunjë - shtyllë metalik	PM
19145	7511247.849	4688312.896	711.773	2	Kunjë - shtyllë metalik	PM
19146	7511272.818	4688267.346	716.036	2	Kunjë - shtyllë metalik	PM
19147	7511275.838	4688259.137	716.718	2	Kunjë - shtyllë metalik	PM
19148	7511288.907	4688238.007	716.149	2	Kunjë - shtyllë metalik	PM
19149	7511290.507	4688229.377	715.422	2	Kunjë - shtyllë metalik	PM
19171	7511309.681	4688463.209	671.475	2	Kunjë - shtyllë metalik	PM
19172	7511302.441	4688473.439	671.086	2	Kunjë - shtyllë metalik	PM
19173	7511300.391	4688476.859	670.996	2	Kunjë - shtyllë metalik	PM
19174	7511285.471	4688488.059	671.696	2	Kunjë - shtyllë metalik	PM
19175	7511274.862	4688496.079	672.155	2	Kunjë - shtyllë metalik	PM
19176	7511265.422	4688501.239	673.081	2	Kunjë - shtyllë metalik	PM
19207	7511294.537	4688234.237	712.707	2	Kunjë - shtyllë metalik	PM
19210	7511250.730	4688377.394	696.917	2	Kunjë - shtyllë metalik	PM
19211	7511246.450	4688366.434	699.259	2	Kunjë - shtyllë metalik	PM
19212	7511279.009	4688329.104	701.278	2	Kunjë - shtyllë metalik	PM
19213	7511294.718	4688270.706	707.846	2	Kunjë - shtyllë metalik	PM
19214	7511295.217	4688252.596	711.245	2	Kunjë - shtyllë metalik	PM
19256	7511281.600	4688417.502	685.163	2	Kunjë - shtyllë metalik	PM
19257	7511261.640	4688392.123	692.813	2	Kunjë - shtyllë metalik	PM
19258	7511218.361	4688403.804	694.937	2	Kunjë - shtyllë metalik	PM
19314	7511245.772	4688461.191	681.751	2	Kunjë - shtyllë metalik	PM
25378	7511294.840	4688242.424	712.215	2	Kunjë - shtyllë metalik	PM

Rilevoi / Snimio: LIRIDON SEJDIU
(emri dhe mbiemri i gjeodetit/kompanisë/ ime i prezime geodeta/ kompanije)

Nr. i licencës / Br. licence: 140

Nënshkrimi / Potpis: _____

Data e rilevimit / Datum snimanja: 18.09.2026

V.V.

Aprovoi / Usvojio: _____
(emri dhe mbiemri i përsonit zyrtar/ ime i prezime sluzbenog lica)

Nënshkrimi / Potpis: _____

Data e aprovimit / Datum usvajanja: _____