



**Republika e Kosovës**  
**Republika Kosova-Republic of Kosova**  
**Qeveria -Vlada-Government**

*Ministria e Mjedisit dhe Planifikimit Hapësinor /Ministarstvo Sredine i Prostornog Planiranja/Ministry of Environment and Spatial Planning*  
AGJENCIA KADASTRALE E KOSOVËS/ KATASTARSKA AGENCIJA KOSOVA/ KOSOVA CADASTRAL AGENCY

Zyra kadastrale komunale / Opštinska katastarska kancelarija: Ferizaj


Nr. i njësisë kadastrale / Br. katastarske jedinice : 01123-0

Zona kadastrale / Katastarska zona: Zaskok

Numri i lëndës / Broj predmeta: 092/2025

Lloji i njësisë kadastrale / Vrsta katastarske jedinice : Parcel

Shkalla e zvoglimit / Razmera plana : 1:1000

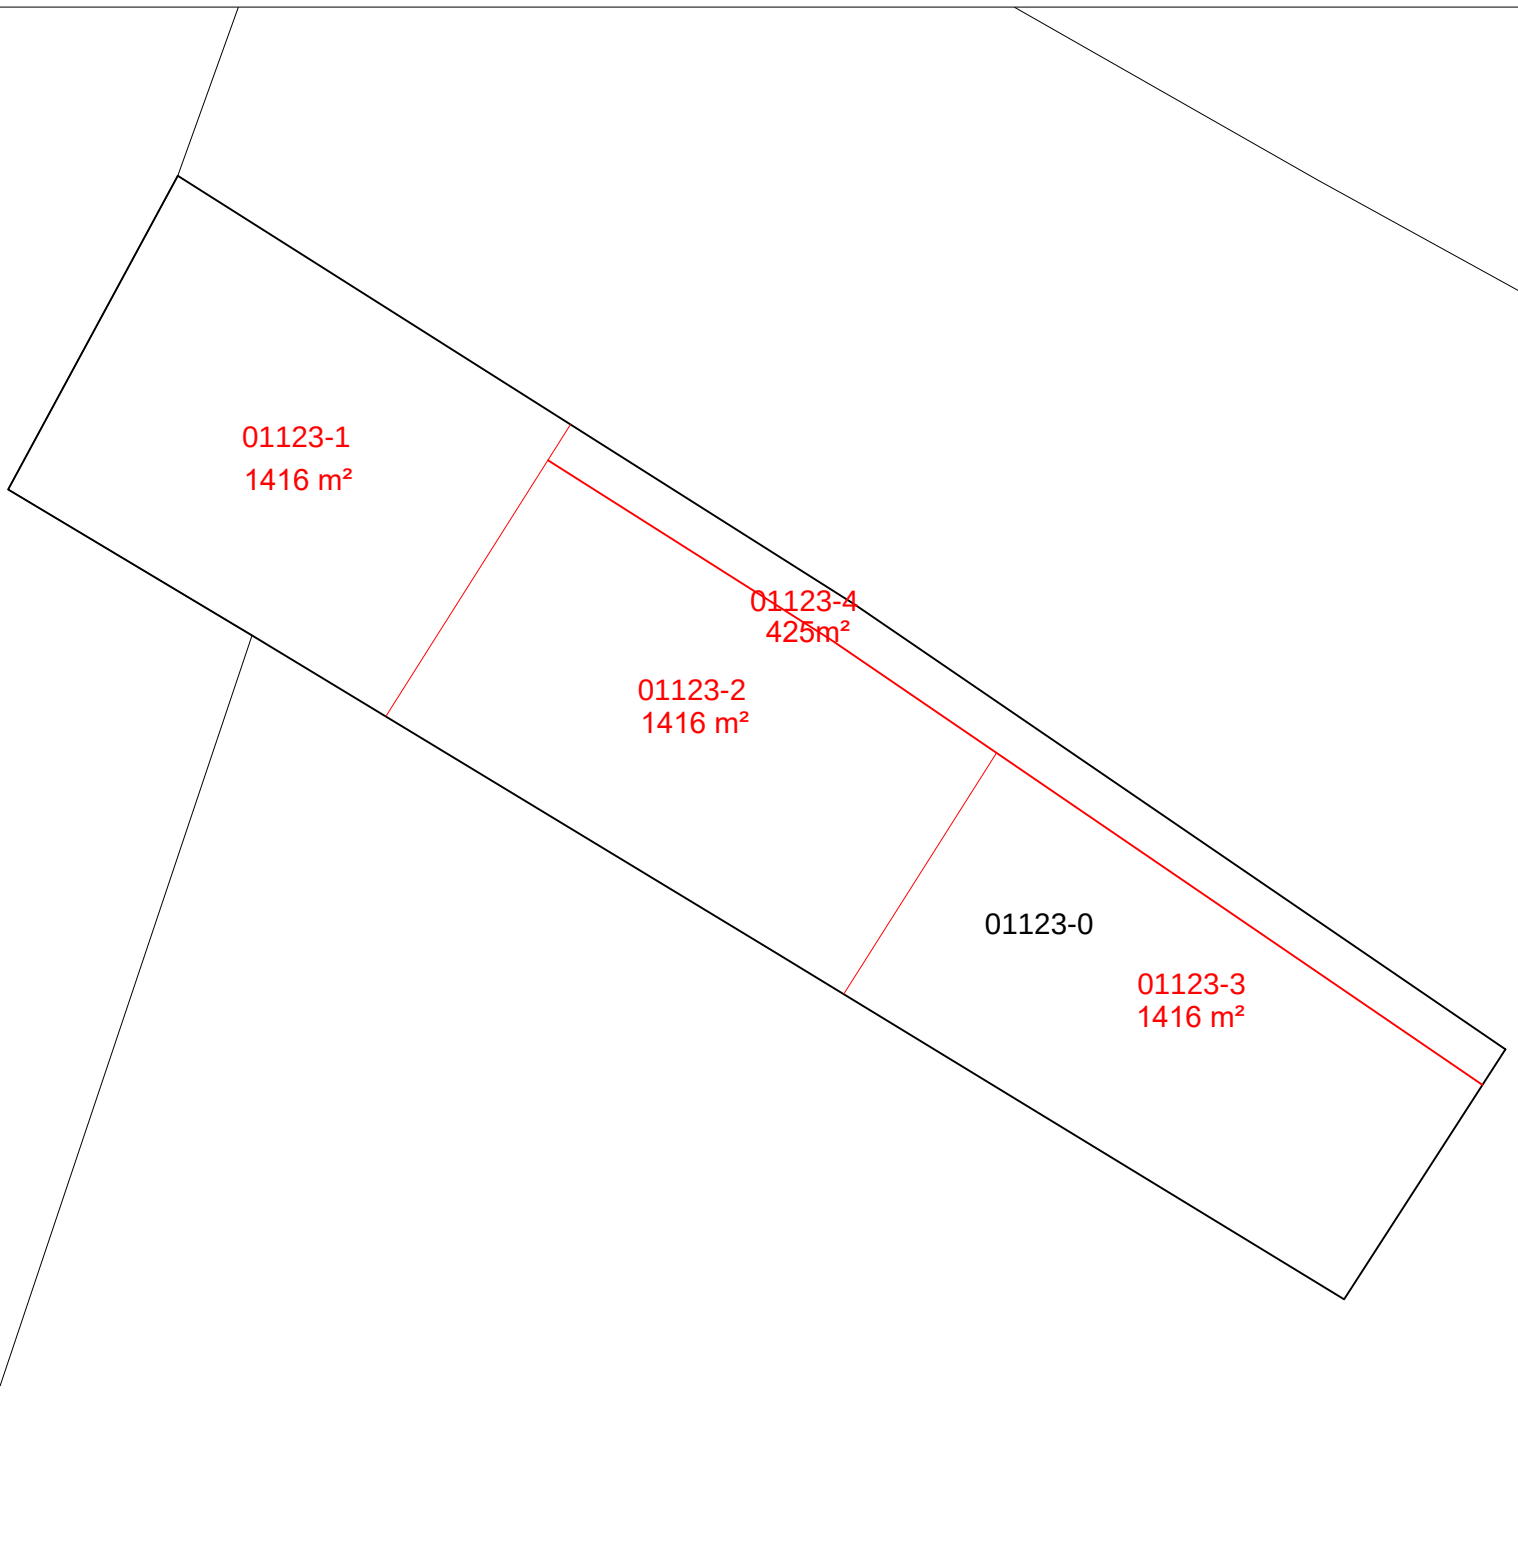

Rilevoi / Snimio: LIRIDON SEJDIU  
(emri dhe mbiemri i gjeodetit/kompanisë/ ime i prezime geodeta/ kompanije)

Aprovoi / Usvojio: \_\_\_\_\_  
(emri dhe mbiemri i përsorit zyrtar/ ime i prezime sluzbenog lica)

Nr. i licencës / Br. licence: 140

V.V.

Nënshkrimi / Potpis: \_\_\_\_\_

Nënshkrimi / Potpis: \_\_\_\_\_

Data e rlevimit / Datum snimanja: 12.04.2025

Data e aprovimit / Datum usvajanja: \_\_\_\_\_